


Structural 3.03


MAIN SLAB VERTICAL REINFORCEMENT

SCALE: 1/36

1in = 3ft

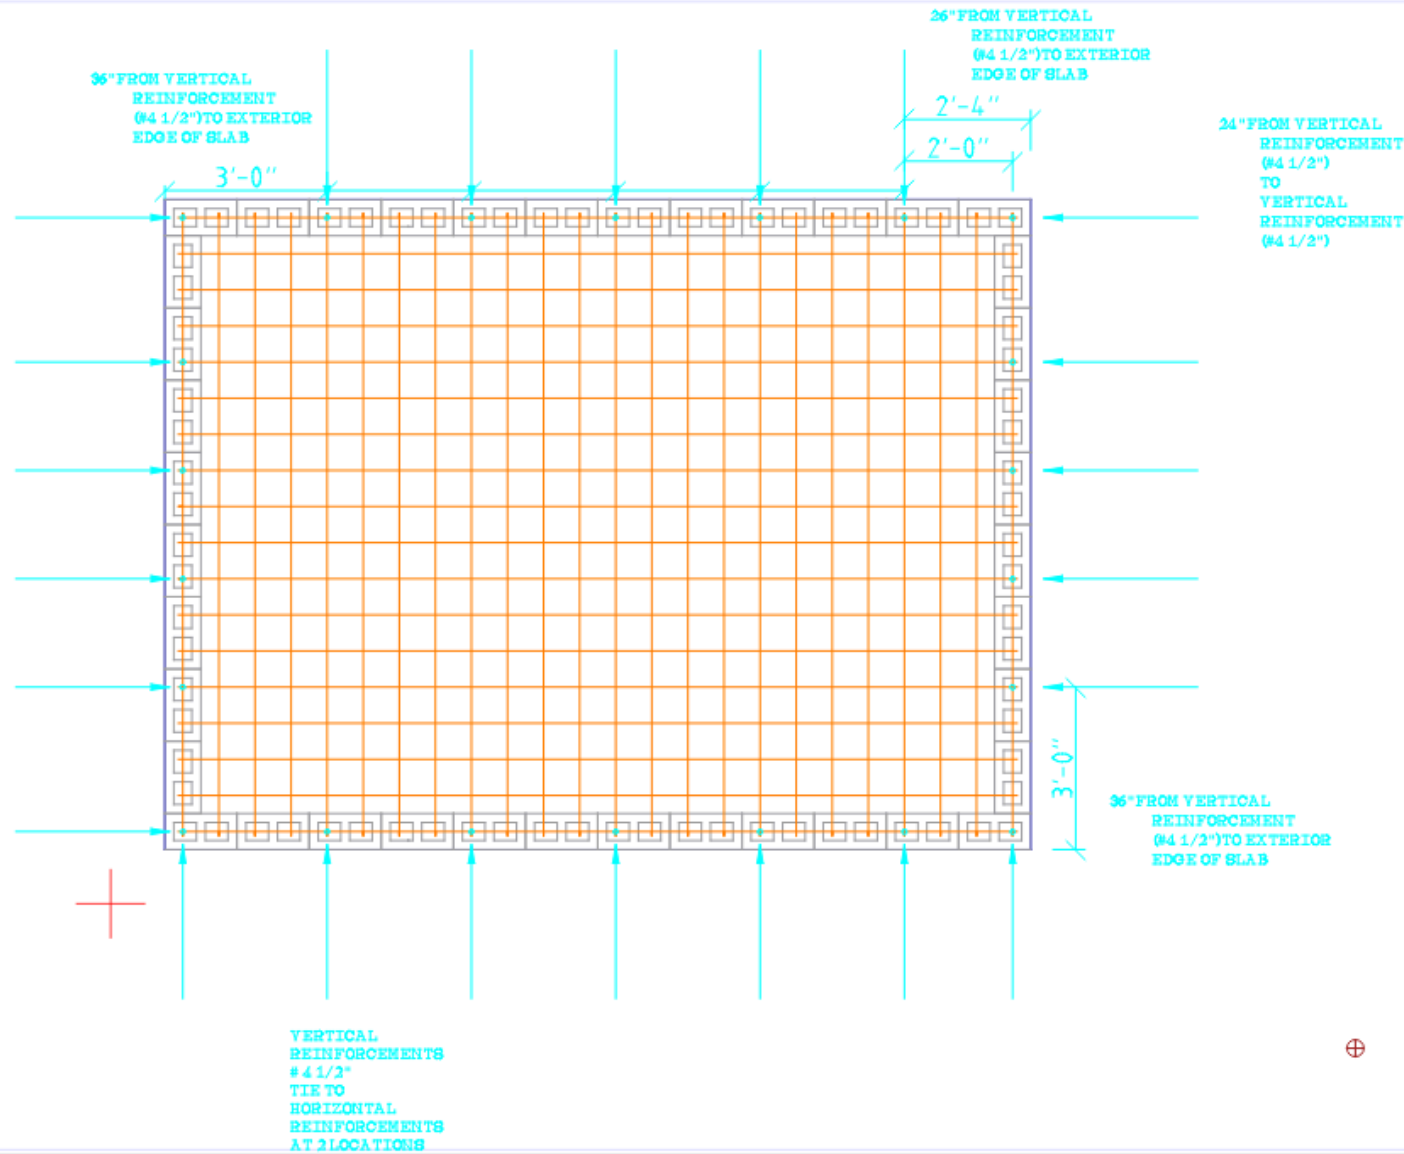

CROSS SECTION DETAIL

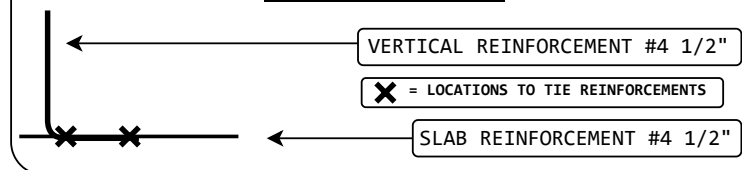

CMU POOL

Cruz Wootten
17575 Parrot Drive
Reno, Nevada
775.501.4398

Structural
S3.03

Drawing
Page
/